


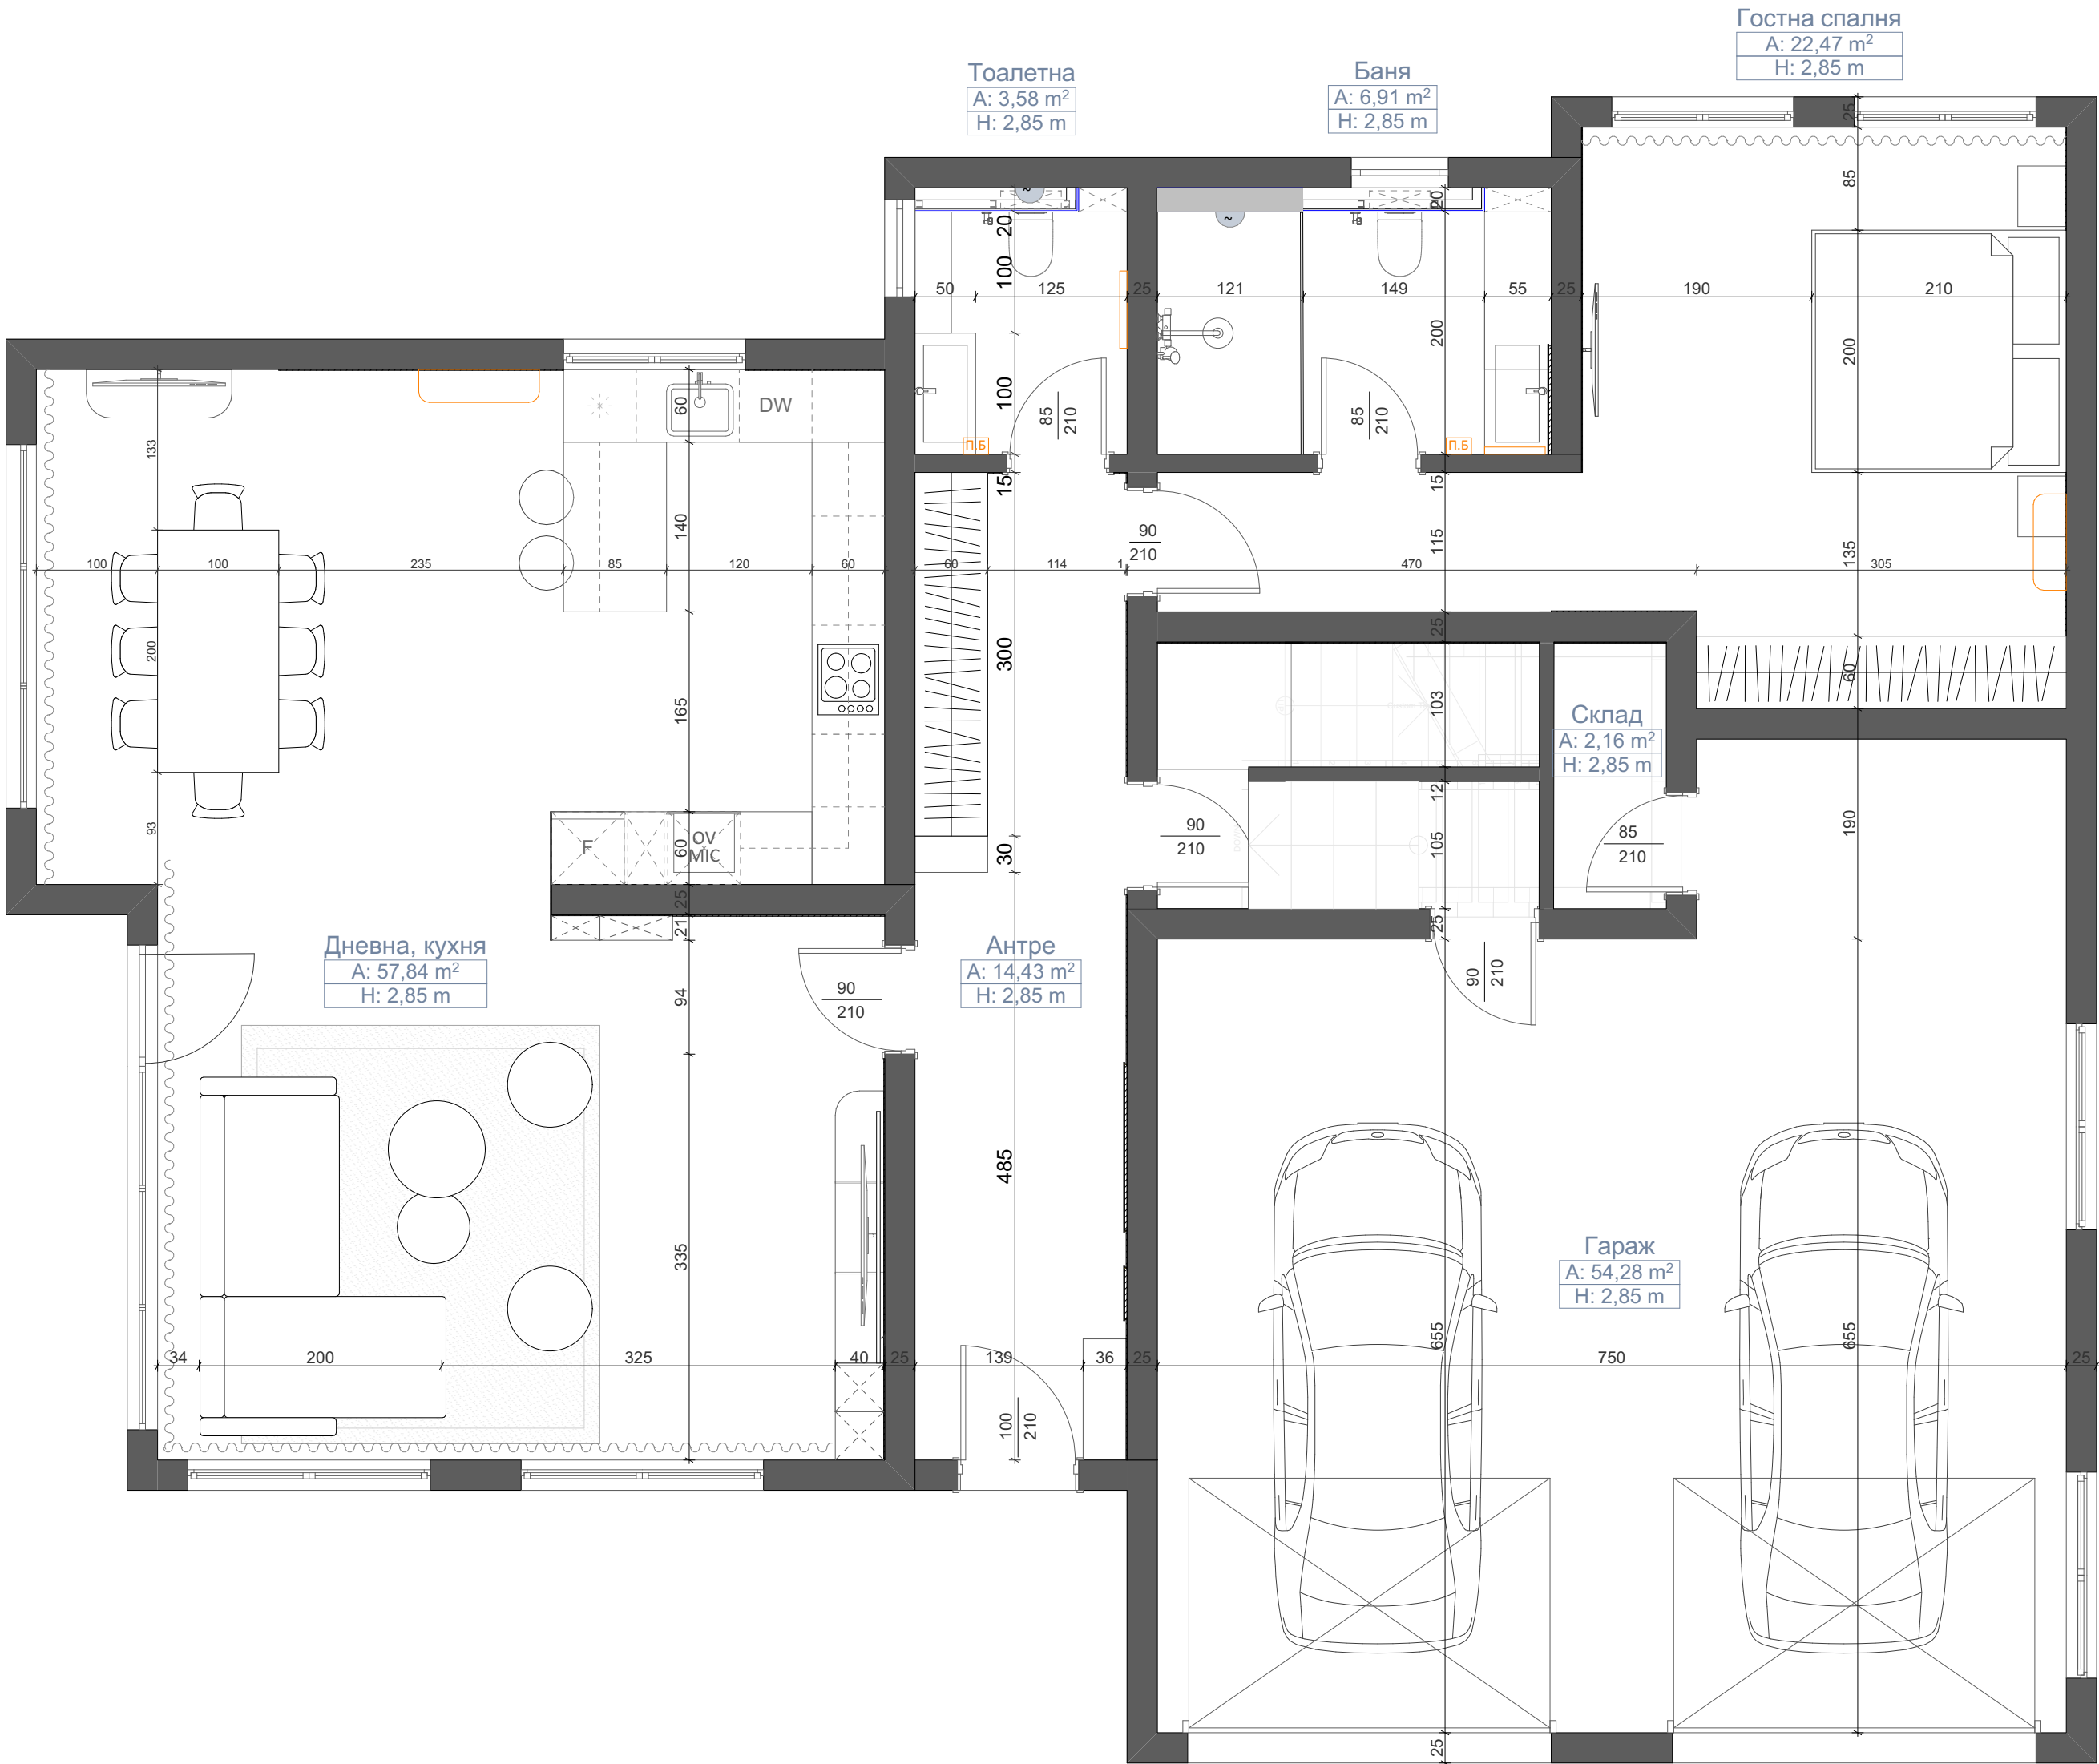

- Легенда:
- Съществуващи стени - тухла
 - Съществуващи стени - тухла
 - Тавани - гипскартон
 - Тавани - влагоустойчив гипскартон
 - Нови предстенни обшивки гипскартон
 - Нови стени / предстенни обшивки - влагоустойчив гипскартон
 - ОВиК уреди
 - Точната позиция, начинът на захранване и монтаж на всички ОВК уреди и съоръжения задължително се определят от правоспособен инженер-проектант и специалист изпълнител по съответната част ОВиК

Забележки:

- Всички размери в чертежа са в сантиметри.
- Проектът е разработен спрямо предоставената архитектурна документация и изпълнение на довършителни работи.
- Всички светли отвори и съществуващи конструктивни елементи подлежат на проверка на място преди започване на работа.
- При необходимост да се сверят позициите на контакти, ключове и изводи с реалните условия и да се уведоми проектанта при разминавания.

ОБЕКТ/ PROJECT NAME: Къща Троян
КЛИЕНТ/ CLIENT: Минко Чолаков
ДАТА / DATE: 4.8.2026 г.