


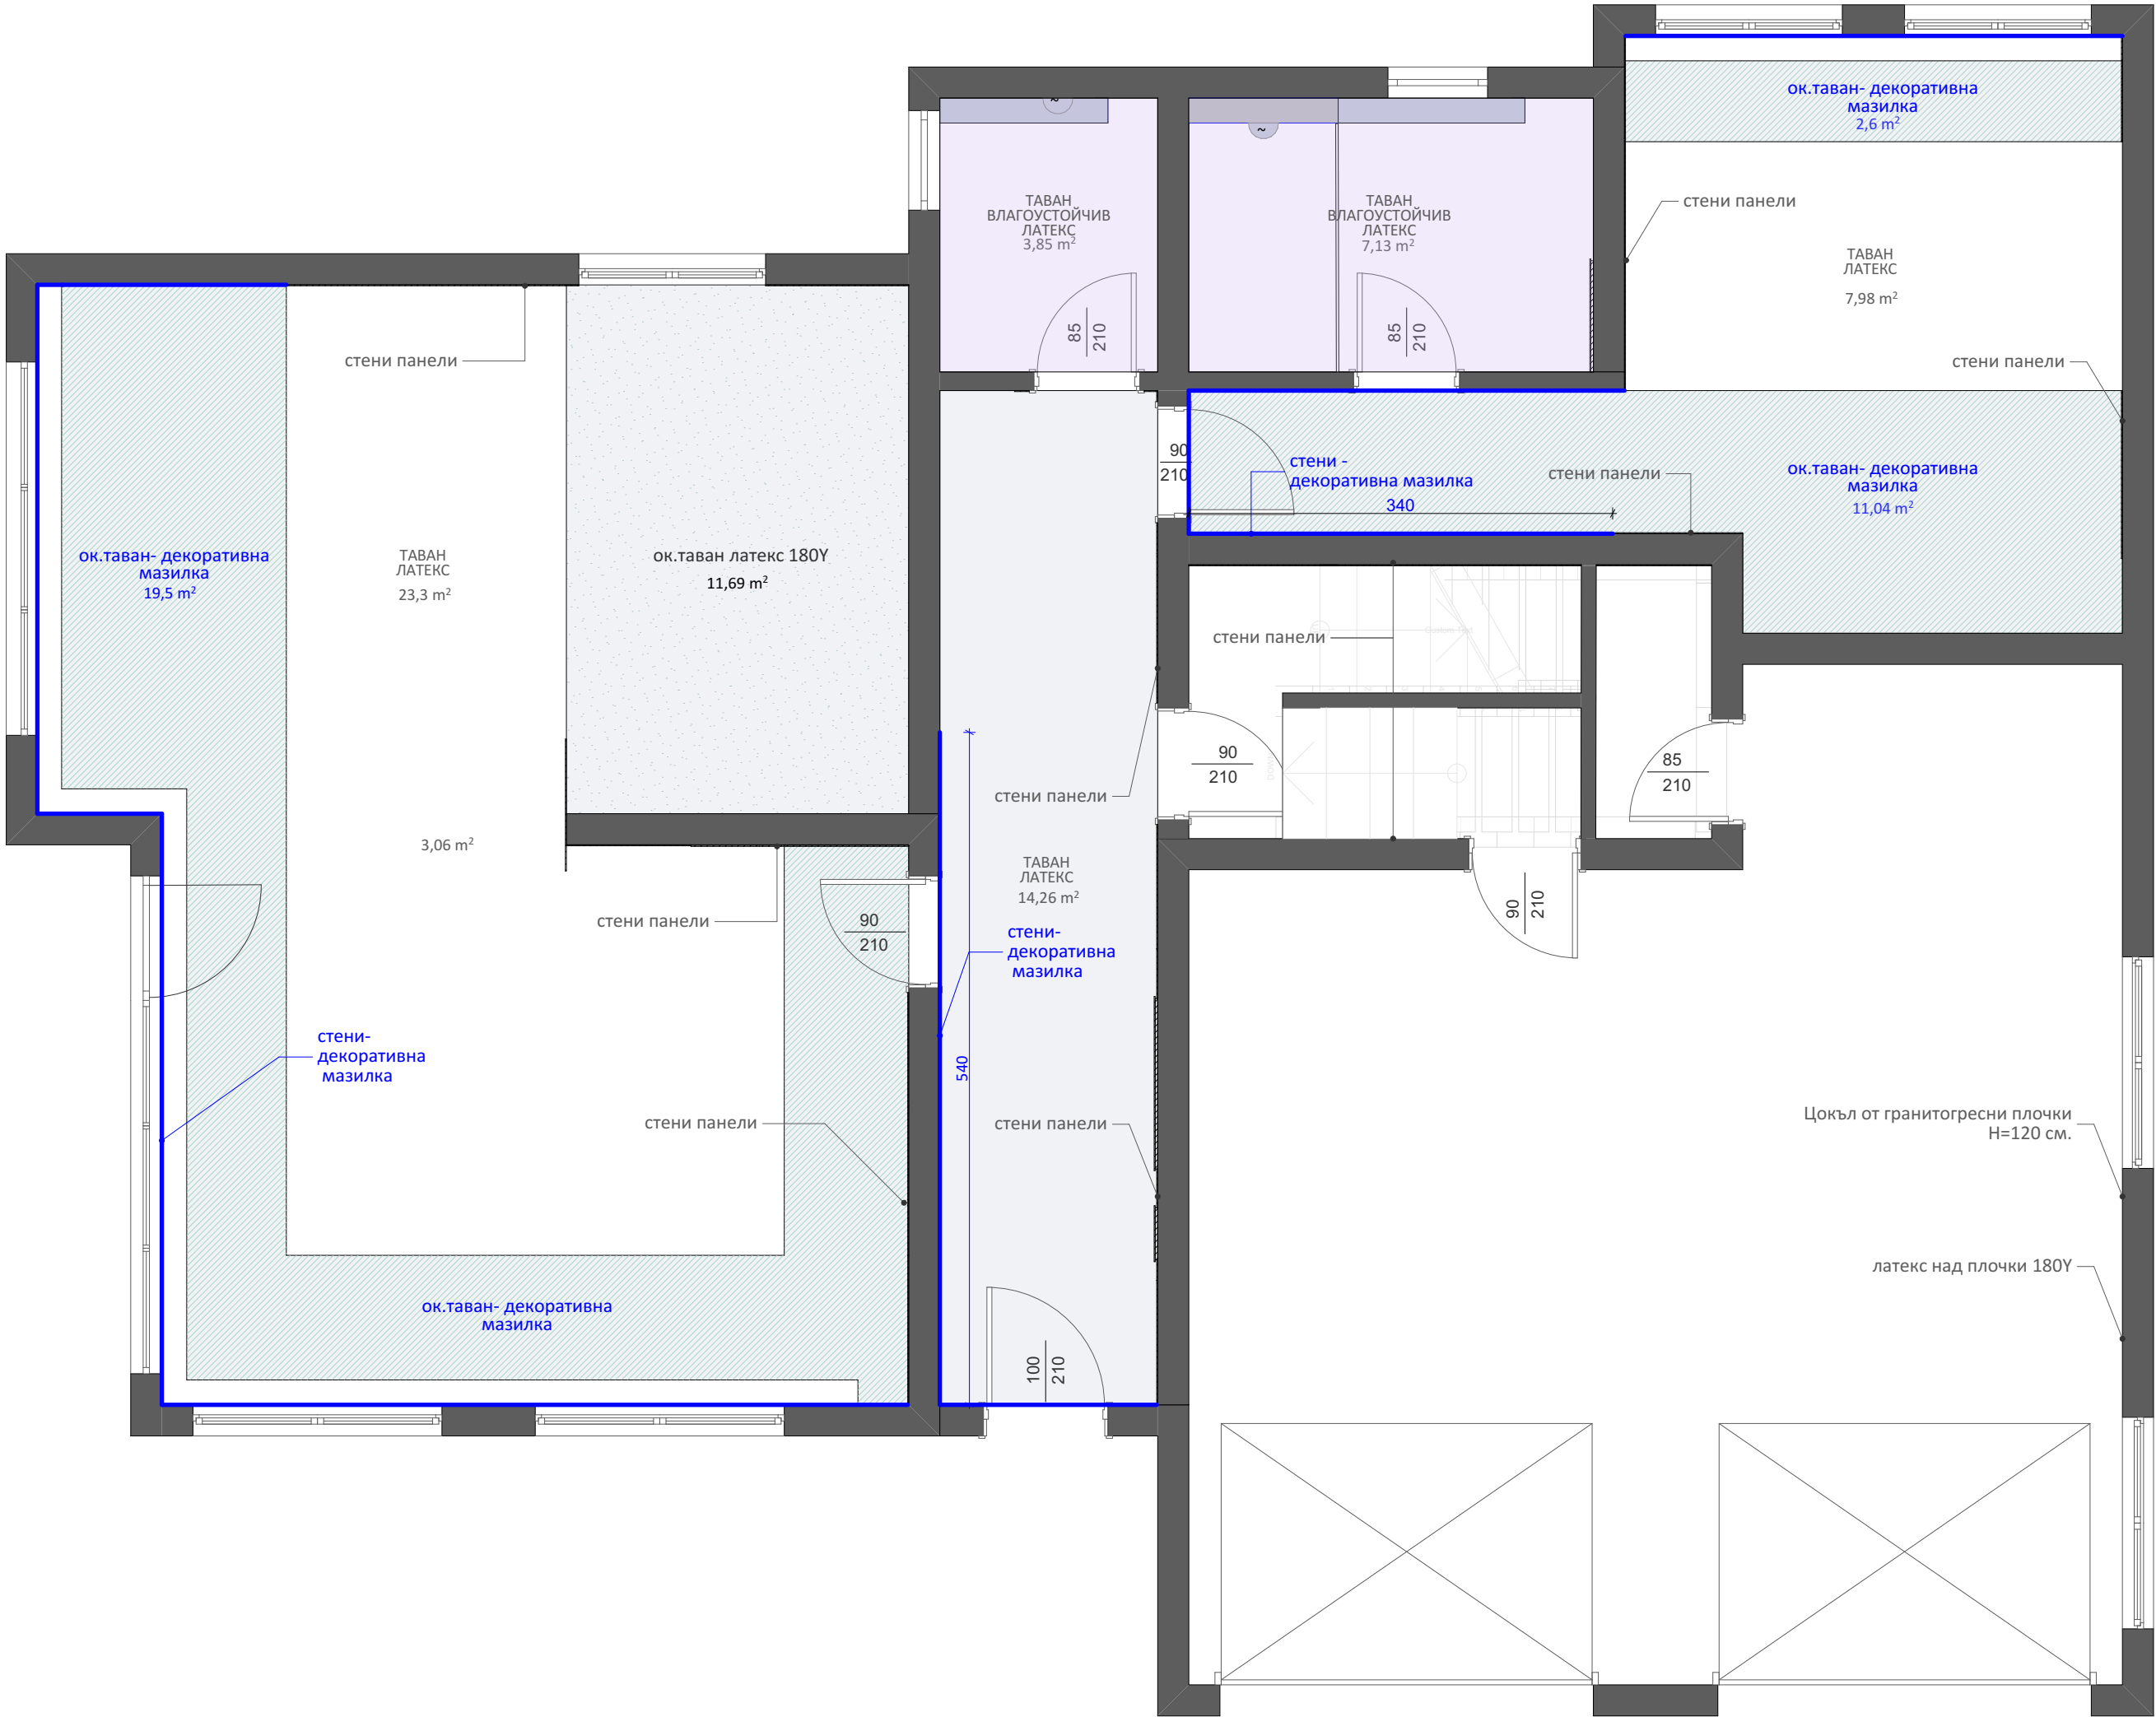

Легенда:

- Декоративна мазилка- San Marco Fontego M143
- Латекс цвят бяло
- Латекс цвят бяло - за влажни помещения
- Латекс цвят бяло - за влажни помещения
- Латекс San Marco 180Y

Забележки:
1. Всички размери в чертежа са в сантиметри.
2. Проектът е разработен спрямо предоставената архитектурна документация и изпълнение на довършителни работи.
3. Всички светли отвори и съществуващи конструктивни елементи подлежат на проверка на място преди започване на работа.
4. При необходимост да се сверят позициите на контакти, ключове и изводи с реалните условия и да се уведоми проектантанта при разминавания.
5. Да се придвиди място за трансформаторите в корусите на мебелите или в ок.тавани , така че да са достъпни.

ОБЕКТ/ PROJECT NAME: Къща Троян
КЛИЕНТ/ CLIENT: Минко Чолаков
ДАТА / DATE: 4.8.2026 г.