


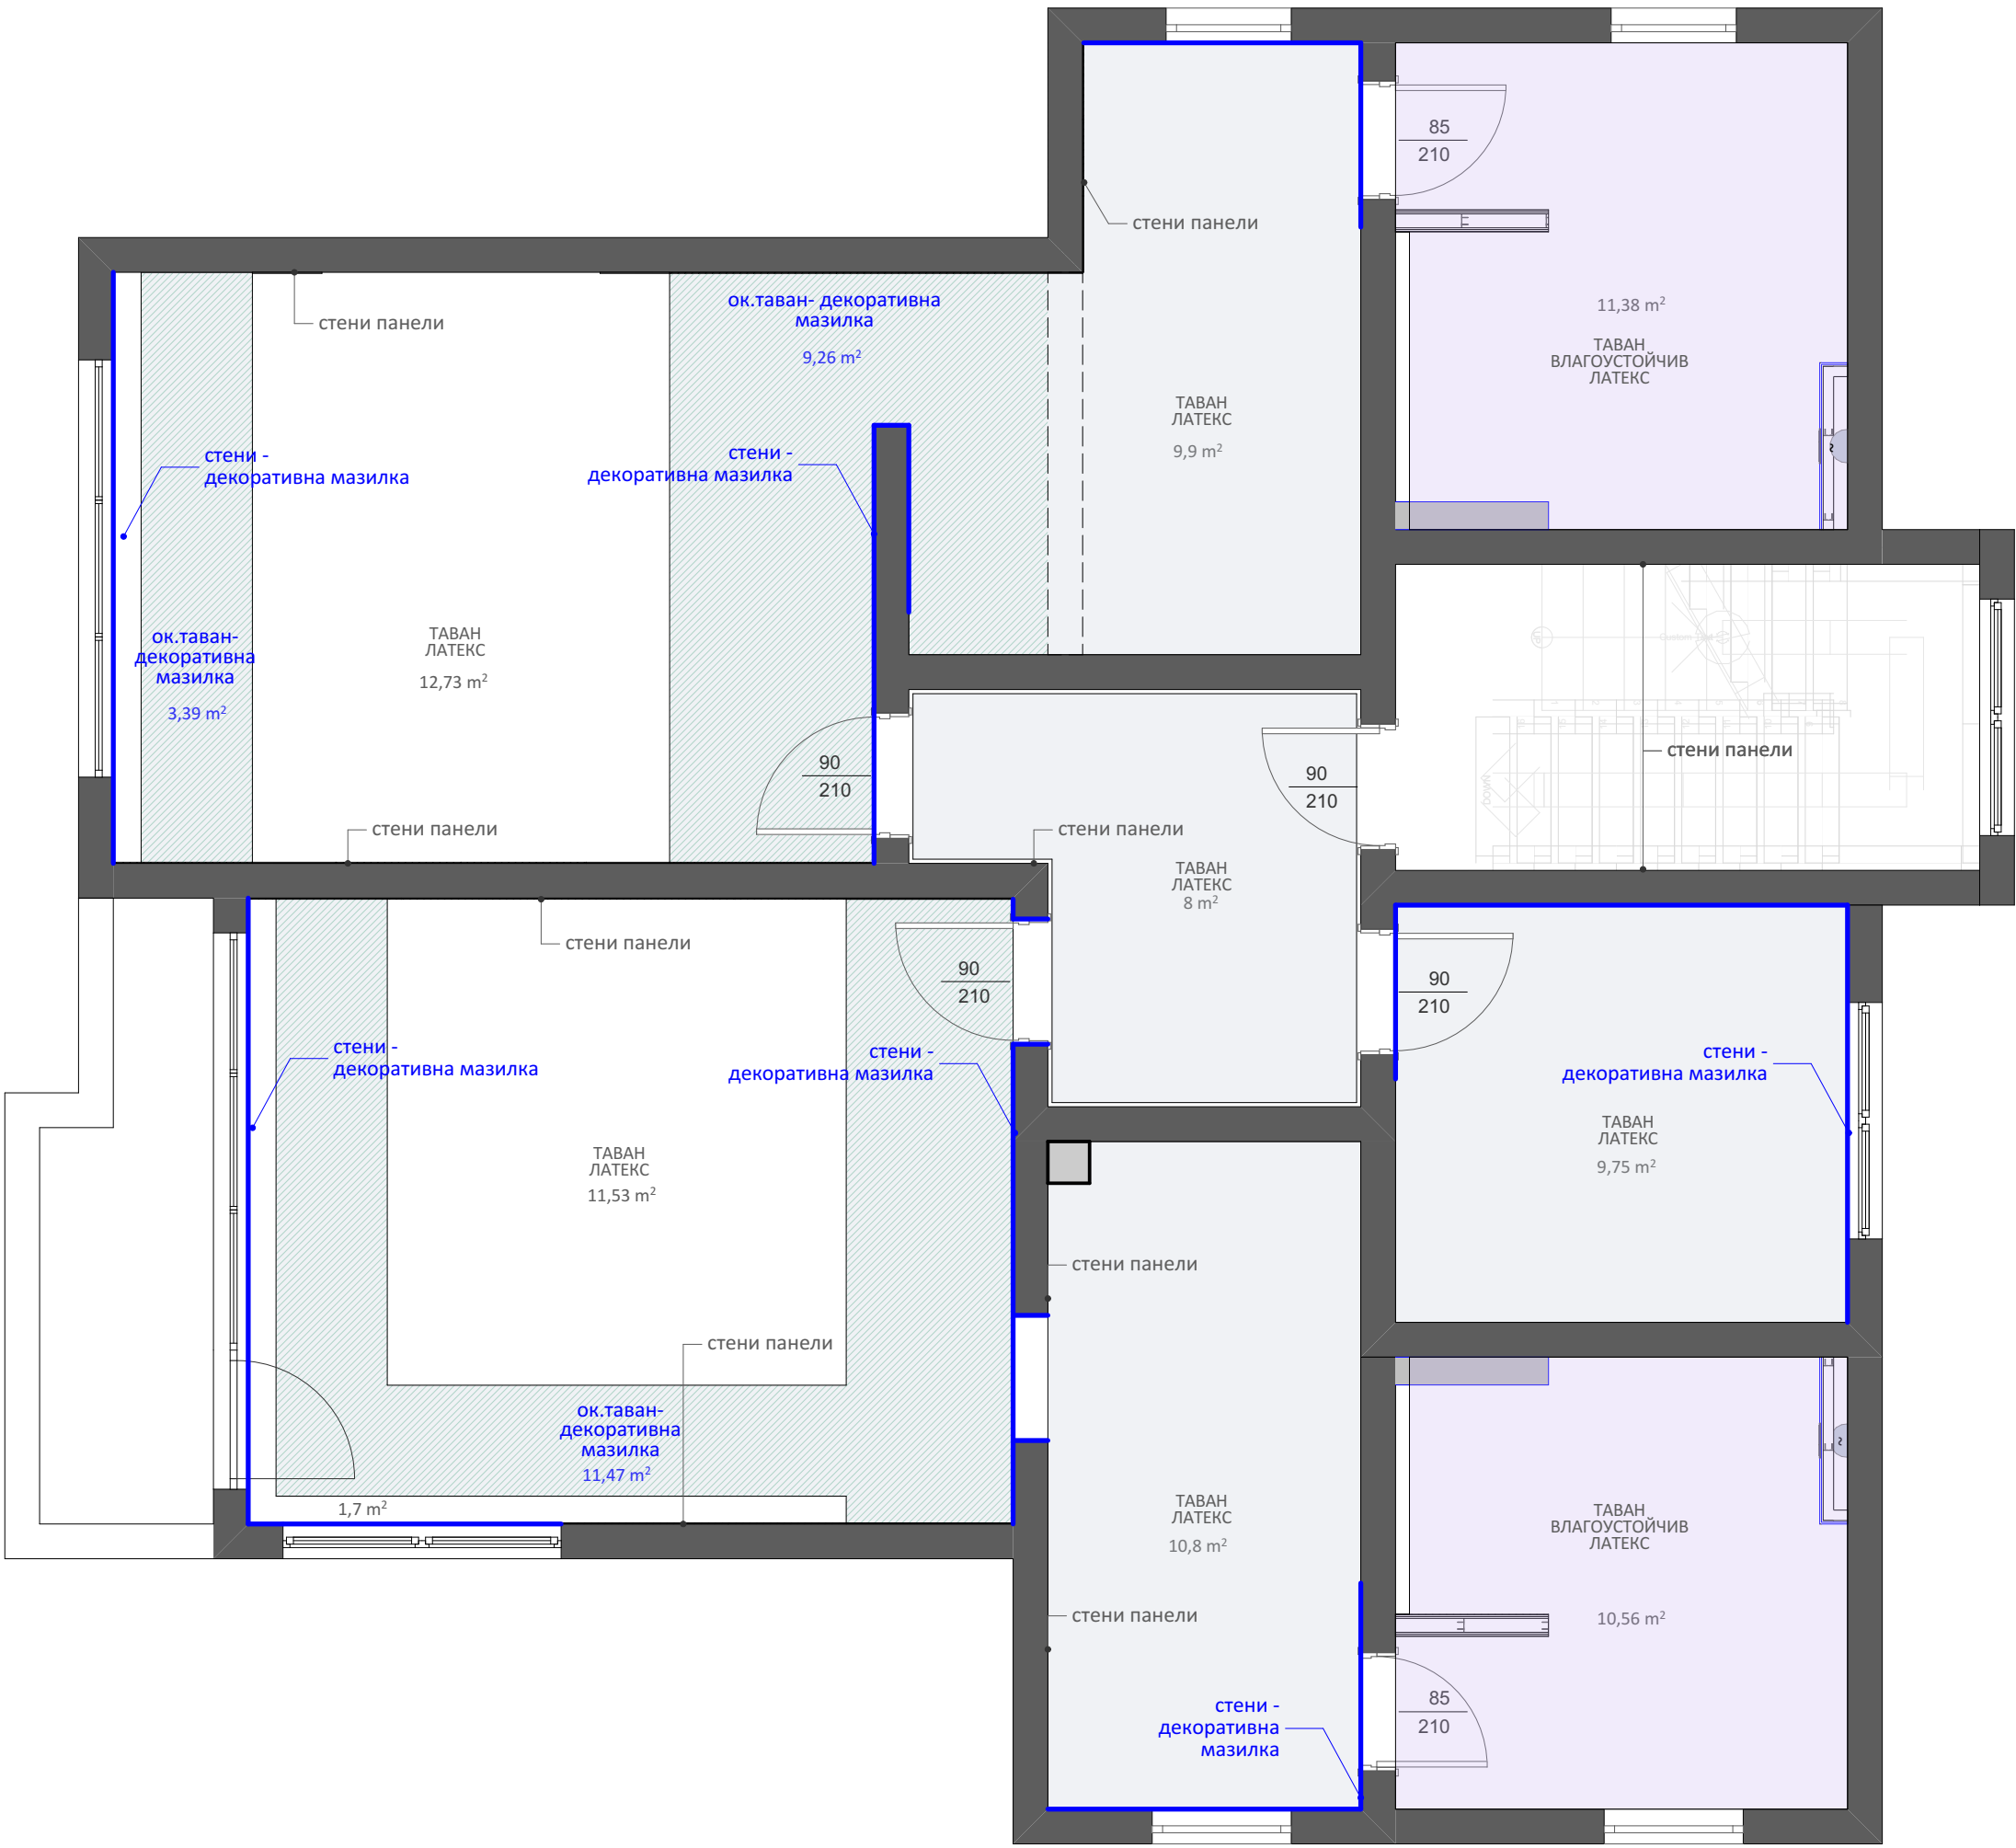

- Легенда:
- Декоративна мазилка- San Marco Fontego M143
 - Латекс цвят бяло
 - Латекс цвят бяло - за влажни помещения
 - Латекс цвят бяло - за влажни помещения
 - Латекс San Marco 180Y

Забележки:

- Всички размери в чертежа са в сантиметри.
- Проектът е разработен спрямо предоставената архитектурна документация и изпълнение на довършителни работи.
- Всички светли отвори и съществуващи конструктивни елементи подлежат на проверка на място преди започване на работа.
- При необходимост да се сверят позициите на контакти, ключове и изводи с реалните условия и да се уведоми проектантанта при разминавания.

ОБЕКТ/ PROJECT NAME: Къща Троян
КЛИЕНТ/ CLIENT: Минко Чолаков
ДАТА / DATE: 4.8.2026 г.