


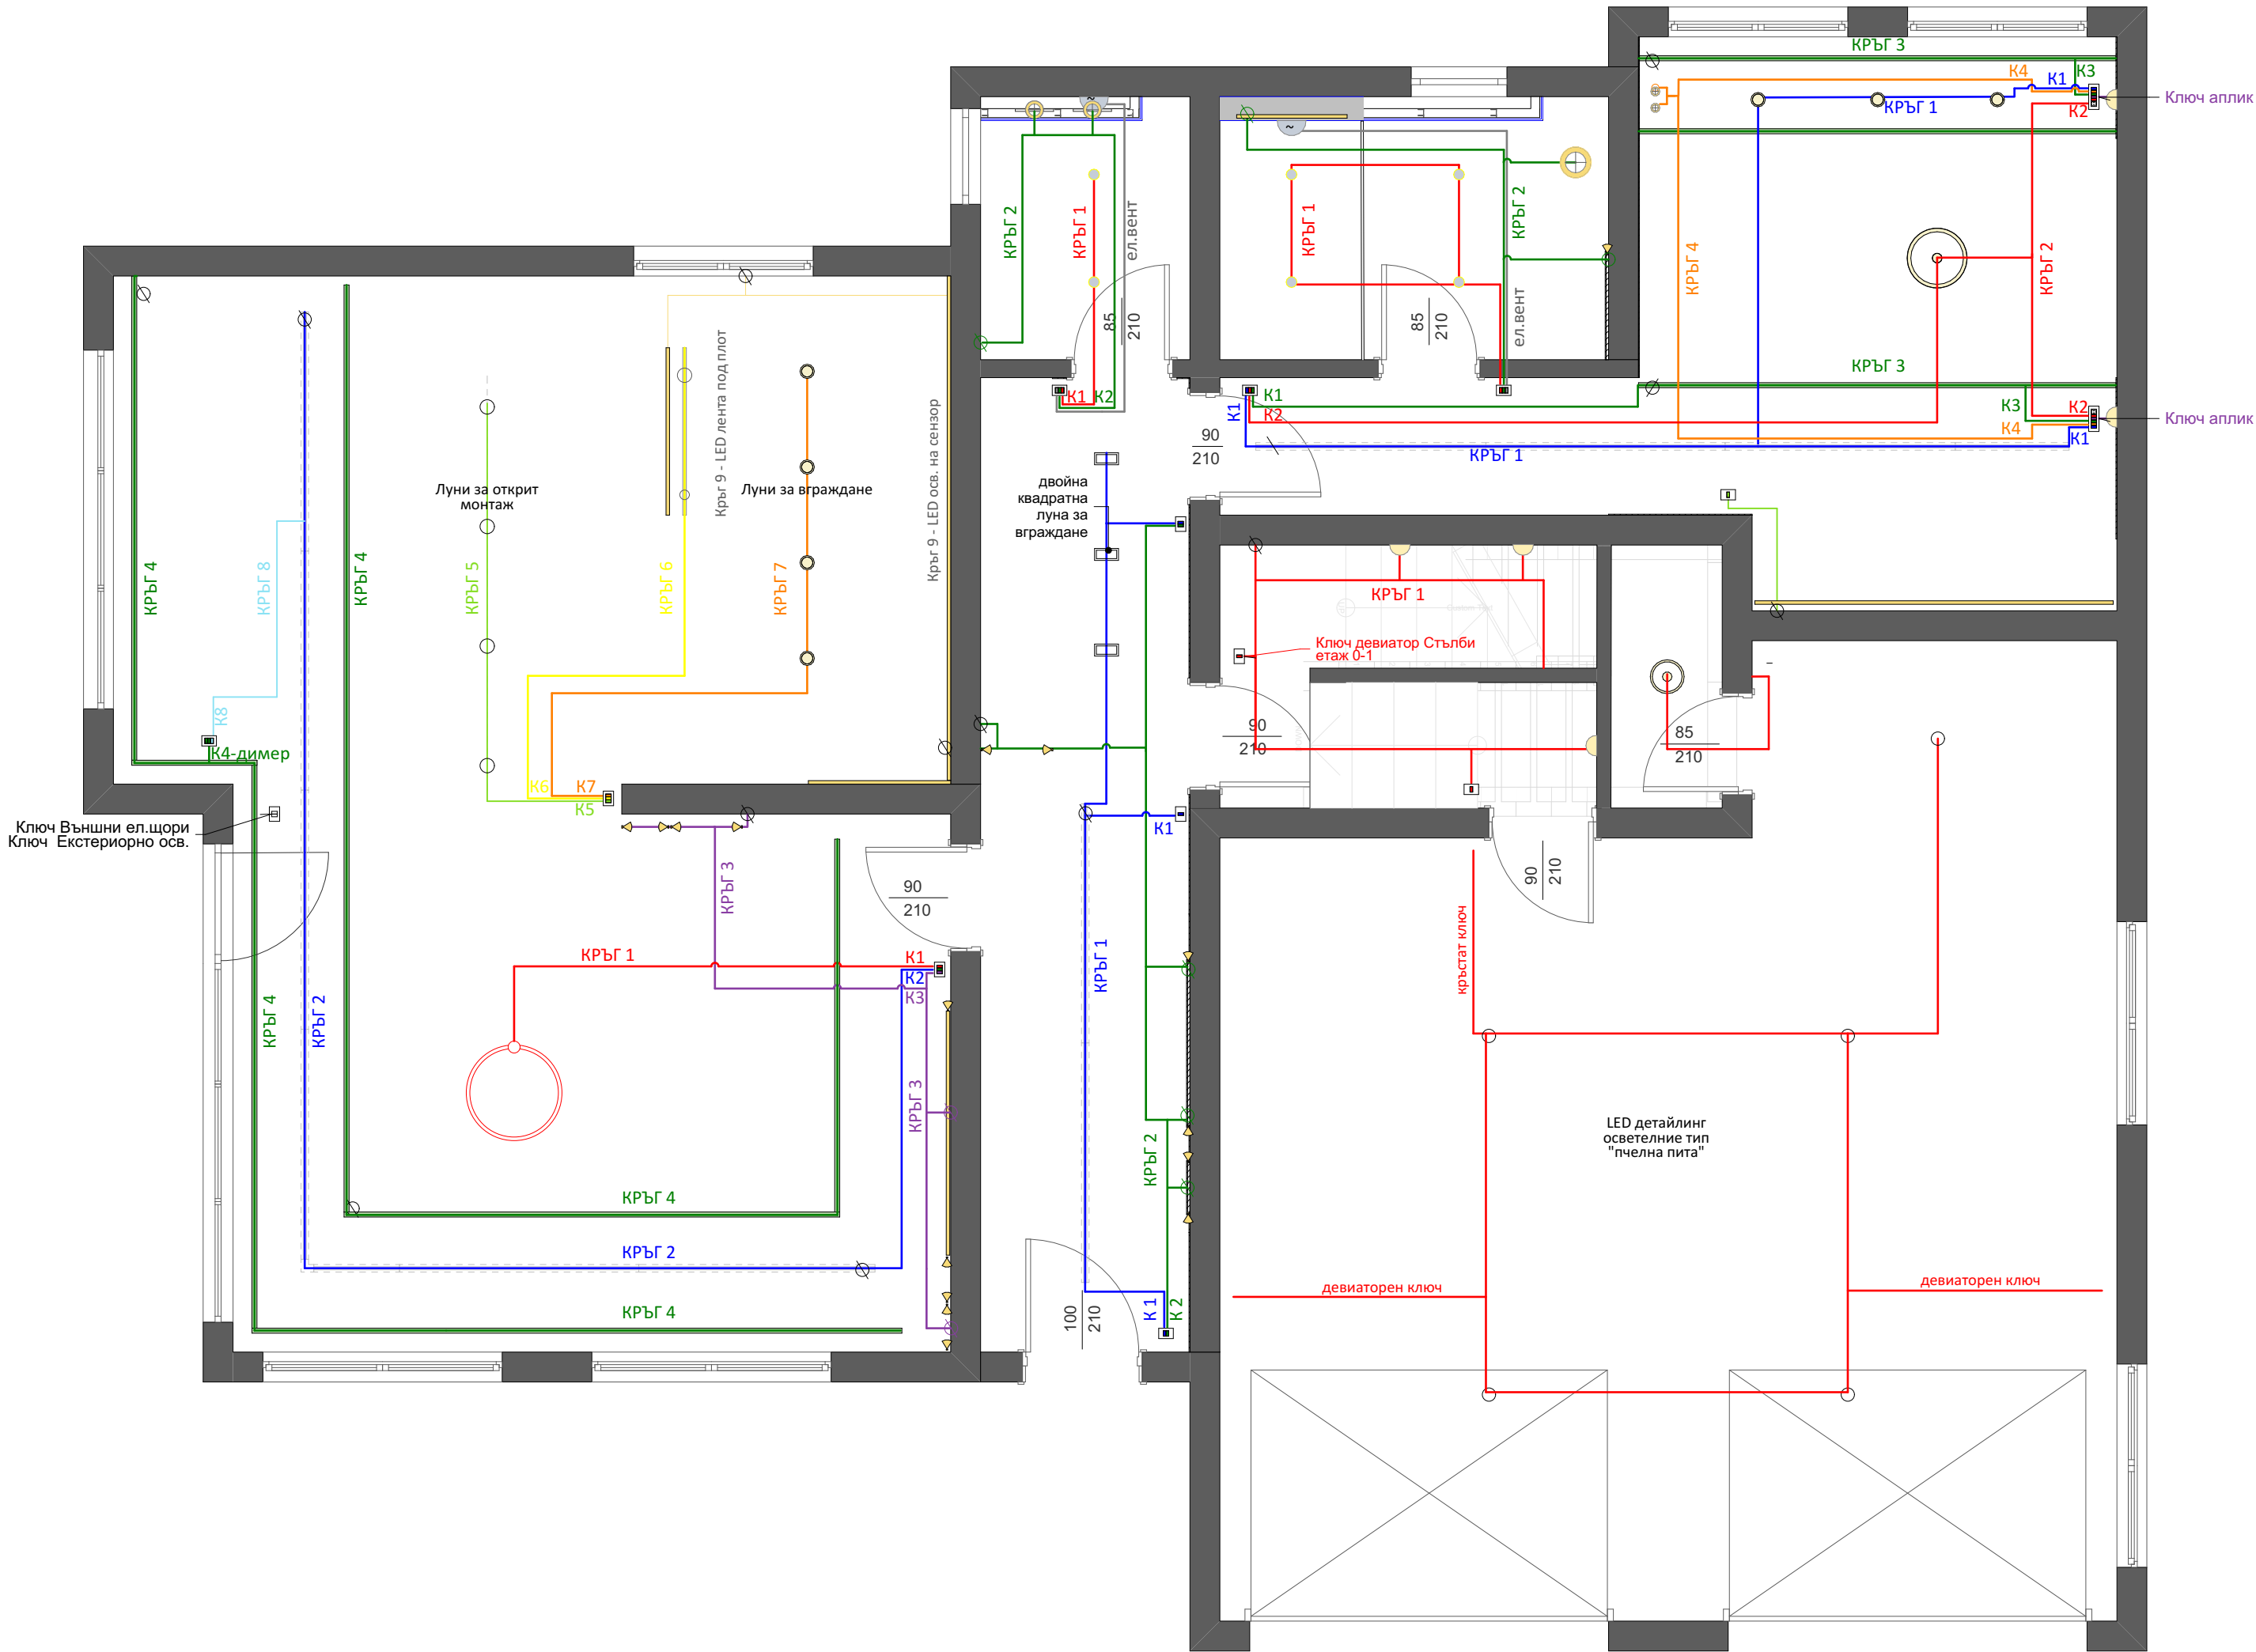

Легенда:

- профил за LED лента за вграждане в мебел хоризонтално бройки във височина
- профил за LED лента за вграждане в мебел вертикално
- LED лента в окачен таван
- LED лента в профил Shadow Gap
- хоризонтална LED лента в гипскартон Влагозащитена
- Магнитна шина за вграждане
- Луна/ Спот за помещения с висока влажност
- Луна Спот за вграждане
- Висяща лампа
- Магнитна шина за вграждане
- Стенна лампа/ Аплик
- Битов вентилатор
- LED осветително тяло за таван
- Плафон
- Извод скрито осв.

- ДНЕВНА:

 - КРЪГ 1 - Плафон Дневна
 - КРЪГ 2 - Магнитна шина за вграждане
 - КРЪГ 3 - Скрито осв. мебели дневна
 - КРЪГ 4 - Скрито осв. ок. таван - димируем
 - КРЪГ 5 - Луни открит монтаж
 - КРЪГ 6 - Висяща лампа кухня
 - КРЪГ 7 - Луни Кухня
 - КРЪГ 8 - Висящи лампи трапезария (в магнитн шина)
 - Кръг 9 - Скрито осв. кухня- на сензор (под горен ред шкафов+под бар плот)
- БАНИ:

 - КРЪГ 1 - Луни в ок. таван
 - КРЪГ 2 - Скрито осв. +висящи лампи
 - КРЪГ 3 - Ел. вентилатор

СПАЛНЯ:

 - КРЪГ 1 - Луни + магнитна шина в ок. таван
 - КРЪГ 2 - Плафон
 - КРЪГ 3 - Скрито осв. ок. таван
 - КРЪГ 4 - Висящи лампи

Забележки:

- Всички размери в чертежа са в сантиметри.
- Проектът е разработен спрямо предоставената архитектурна документация и изпълнение на довършителни работи.
- Всички светли отвори и съществуващи конструктивни елементи подлежат на проверка на място преди започване на работа.
- При необходимост да се сверят позициите на контакти, ключове и изводи с реалните условия и да се уведоми проектантанта при разминавания.
- Да се придвиди място за трансформаторите в корусите на мебелите или в ок.тавани , така че да са достъпни.

ОБЕКТ/ PROJECT NAME: Къща Троян
КЛИЕНТ/ CLIENT: Минко Чолаков
DATA / DATE: 4.8.2026 г.