


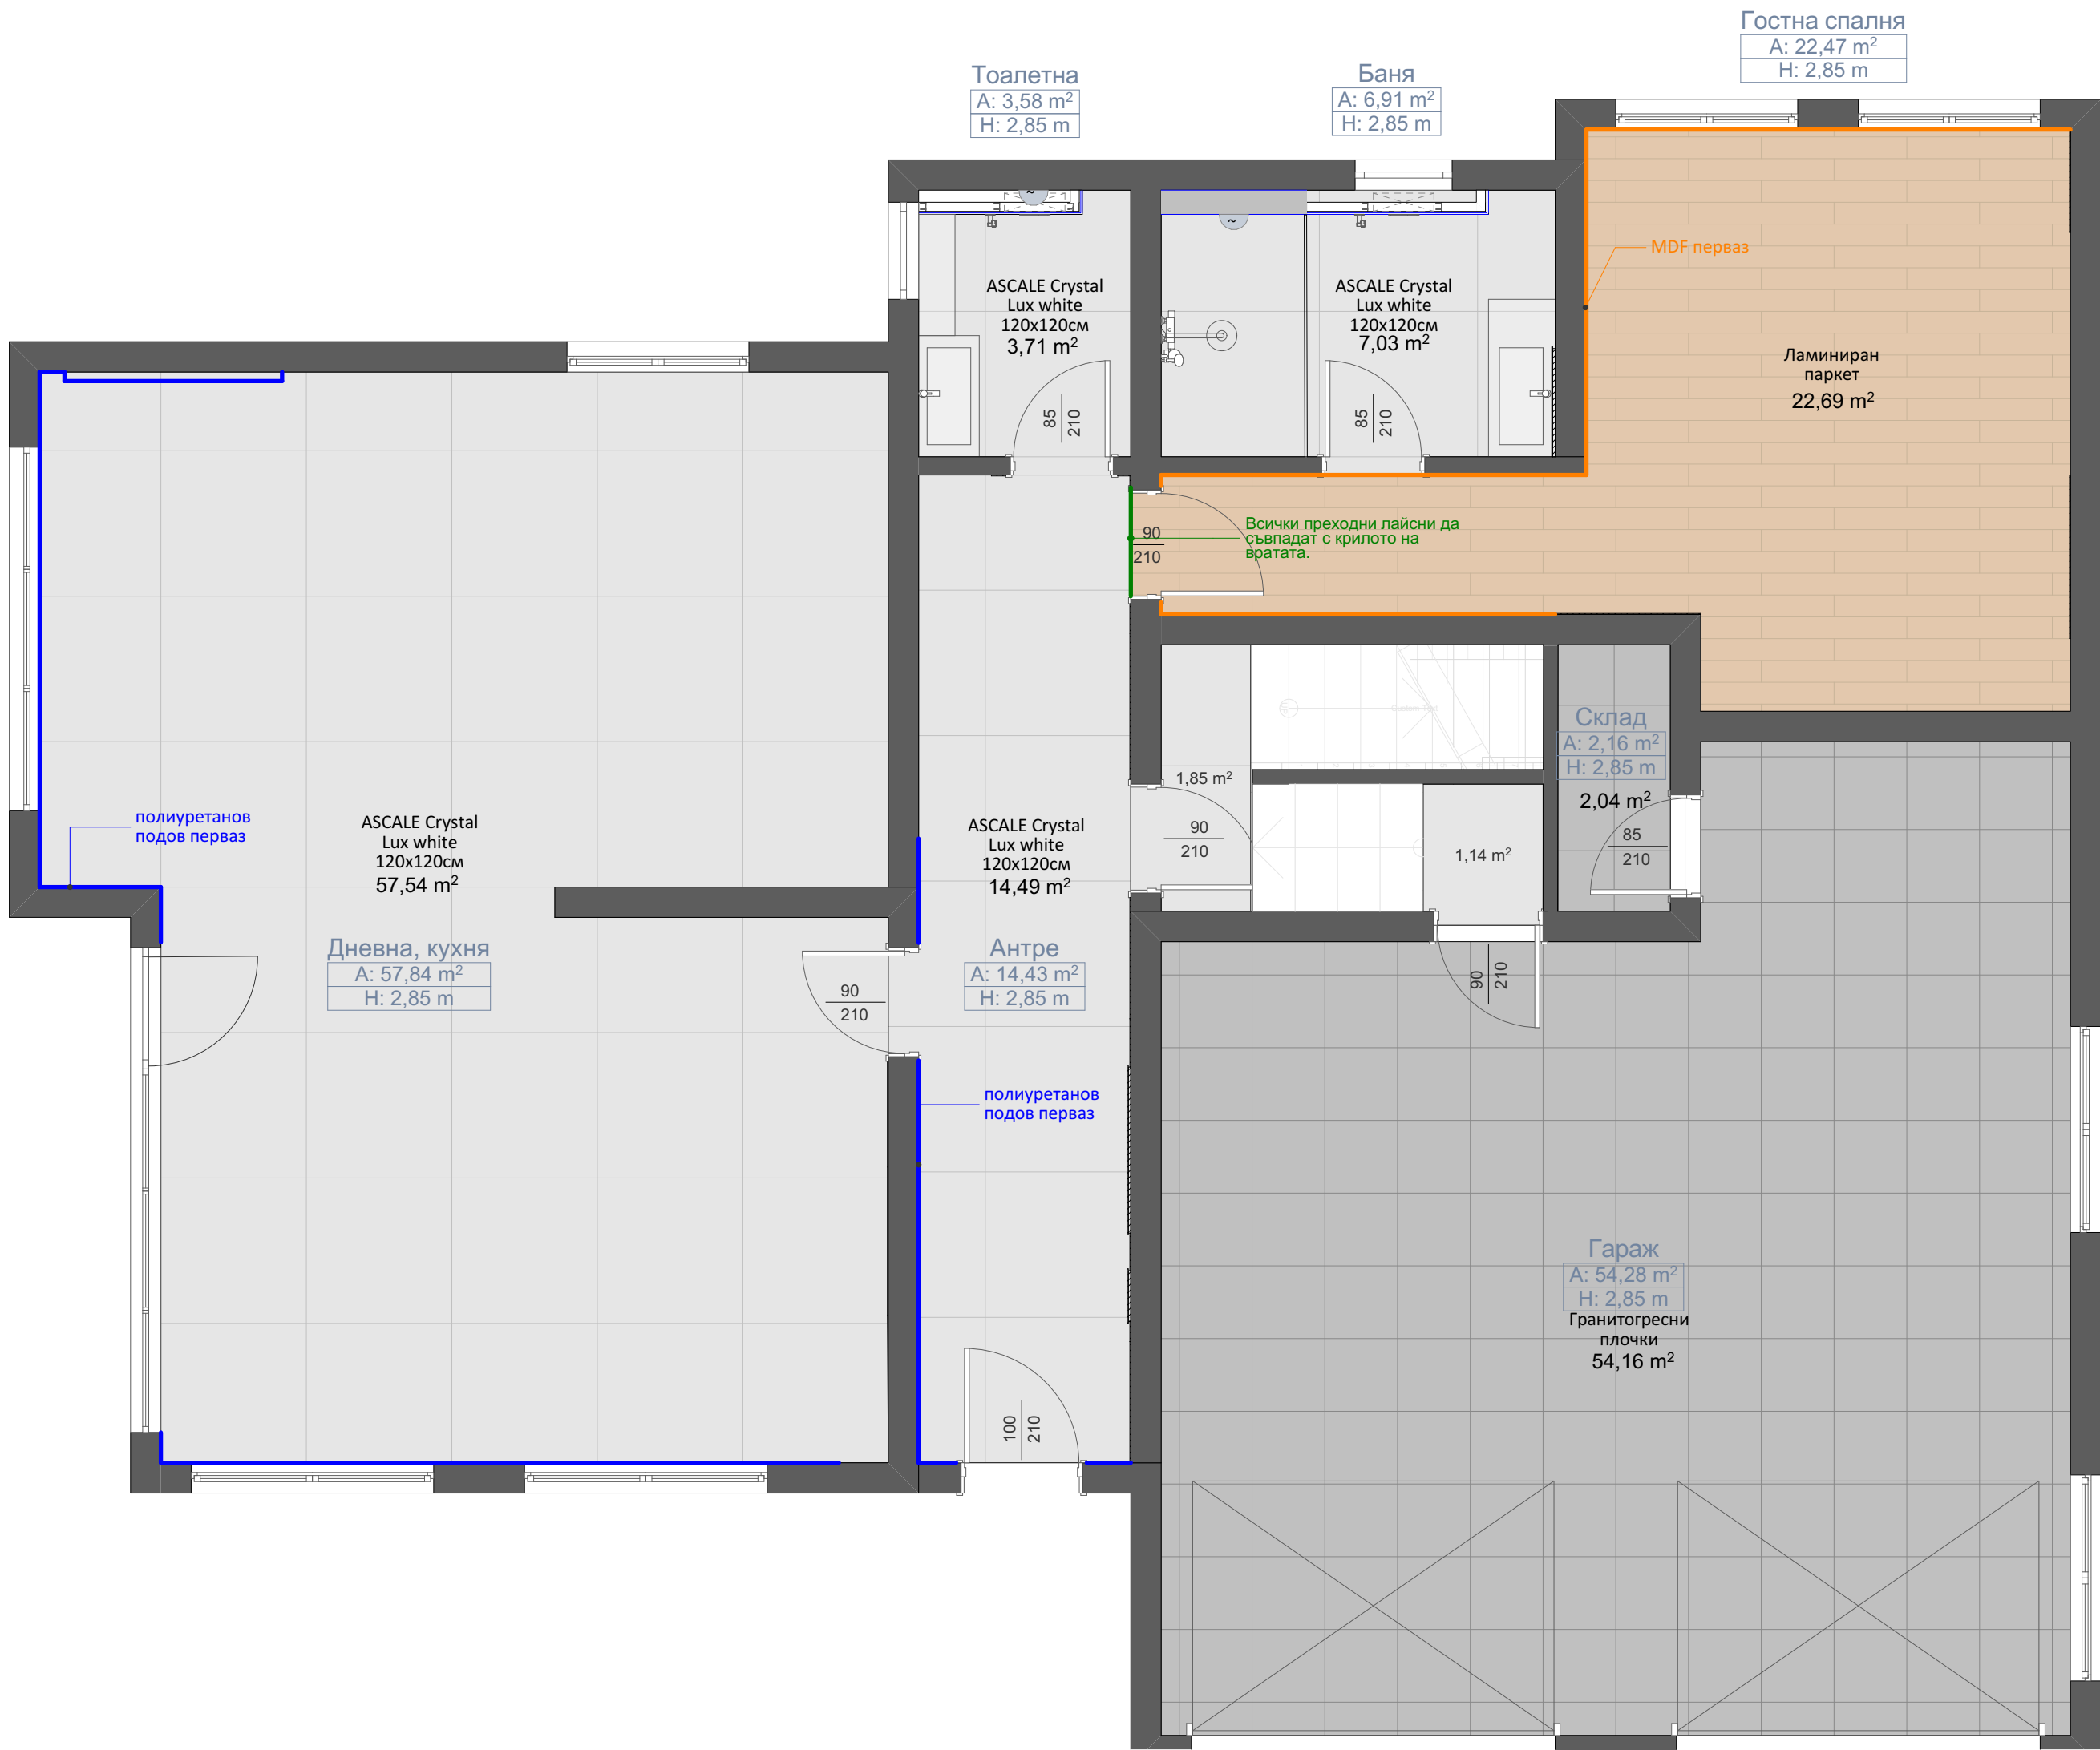

Легенда:

- Ламиниран паркет
- АСCALE Crystal Lux White
- Гранитогресни плочки
- Преходна лайсна между две различни настилки
- Подов перваз MDF
- Полиуретанов перваз

Забележки:
1. Всички размери в чертежа са в сантиметри.
2. Проектът е разработен спрямо предоставената архитектурна документация и изпълнение на довършителни работи.
3. Всички светли отвори и съществуващи конструктивни елементи подлежат на проверка на място преди започване на работа.
4. При необходимост да се сверят позициите на контакти, ключове и изводи с реалните условия и да се уведоми проектантанта при разминавания.

ОБЕКТ/ PROJECT NAME: Къща Троян
КЛИЕНТ/ CLIENT: Минко Чолаков
ДАТА / DATE: 4.8.2026 г.