


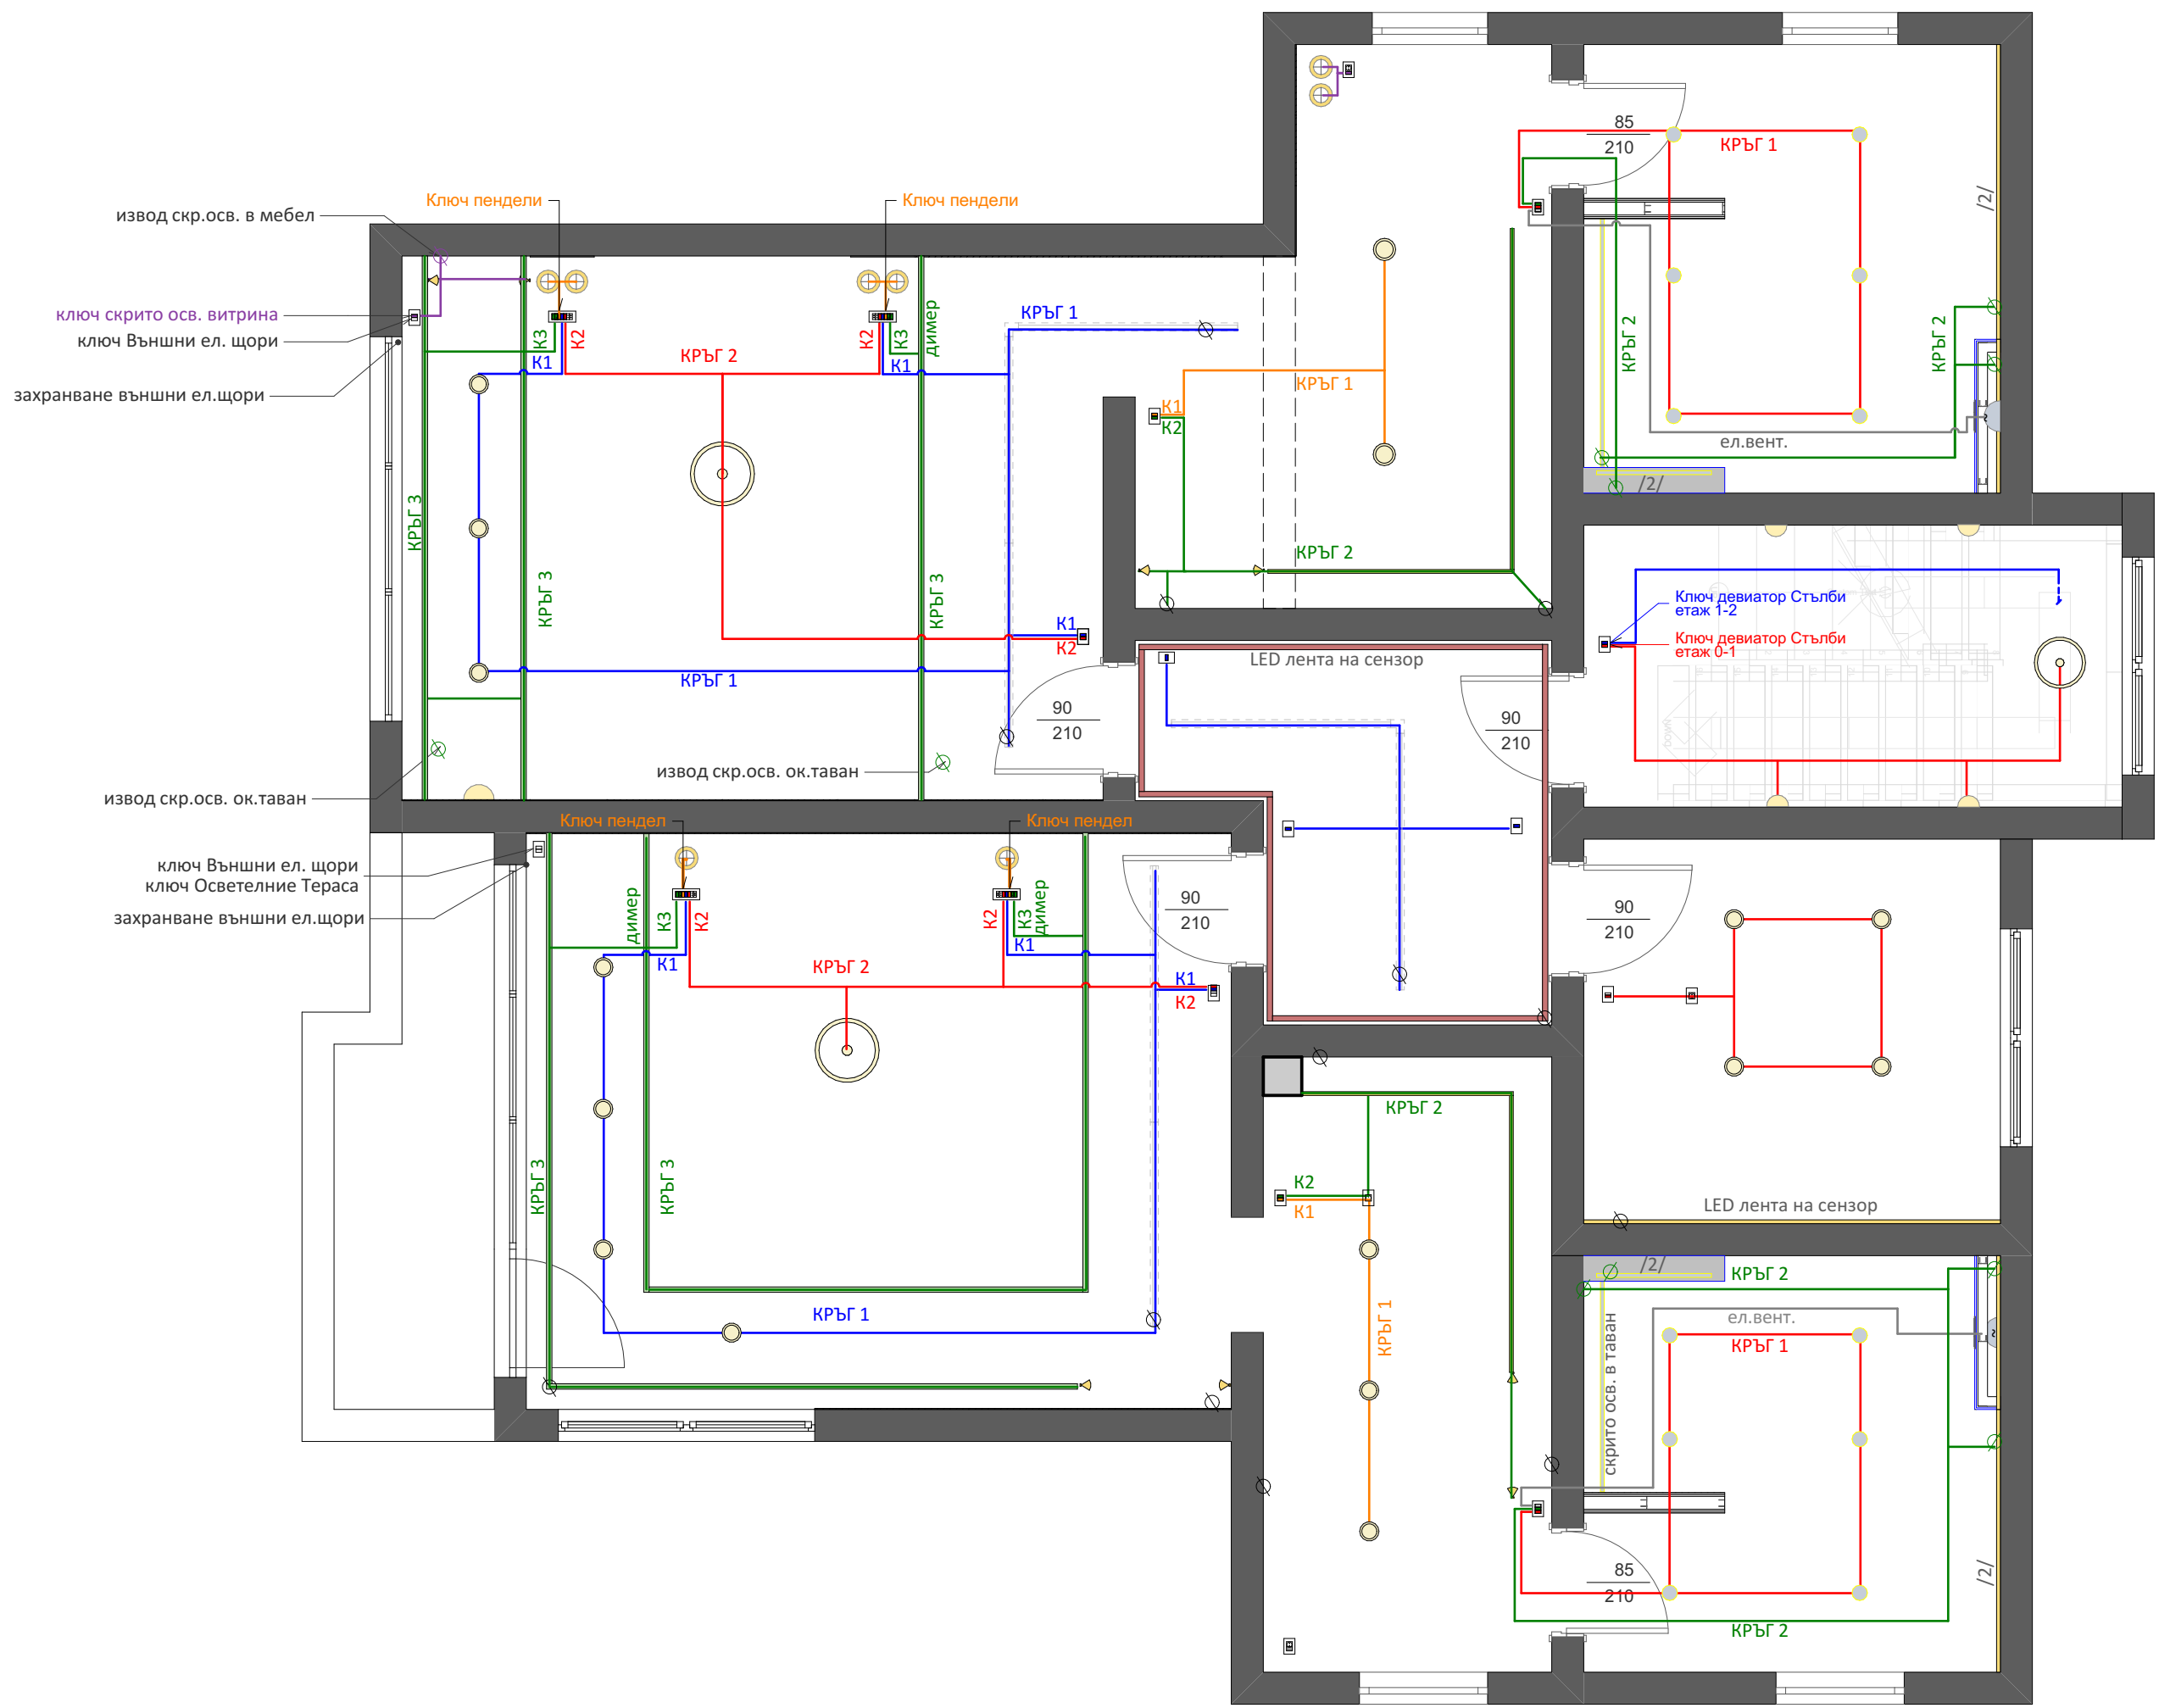

- Легенда:

- | | |
|---|---|
|  | профил за LED лента за вграждане в мебел хоризонтално |
|  | бройки във височина |
|  | |
|  | |
Забележки:

1. Всички размери в чертежа са в сантиметри.
2. Проектът е разработен спрямо предоставената архитектурна документация и изпълнение на довършителни работи.
3. Всички светли отвори и съществувачи конструктивни елементи подлежат на проверка на място преди започване на работа.
4. При необходимост да се свертят позиции на контакти, ключове и изводи с реалните условия и да се уведоми проектантанта при разминавания.
5. Да се придвижи място за трансформаторите в корусите на мебелите или в ок.тавани , така че да са достъжни.

ОБЕКТ/ PROJECT NAME: Къща Троян
КЛИЕНТ/ CLIENT: Минко Чолаков
ДАТА / DATE: 4.8.2026 г.